


02 • Пароводяной контур и механический привод

Эскиз / 08.10.2026 / Не монтажная схема / Уставки и характеристики по паспорту оборудования

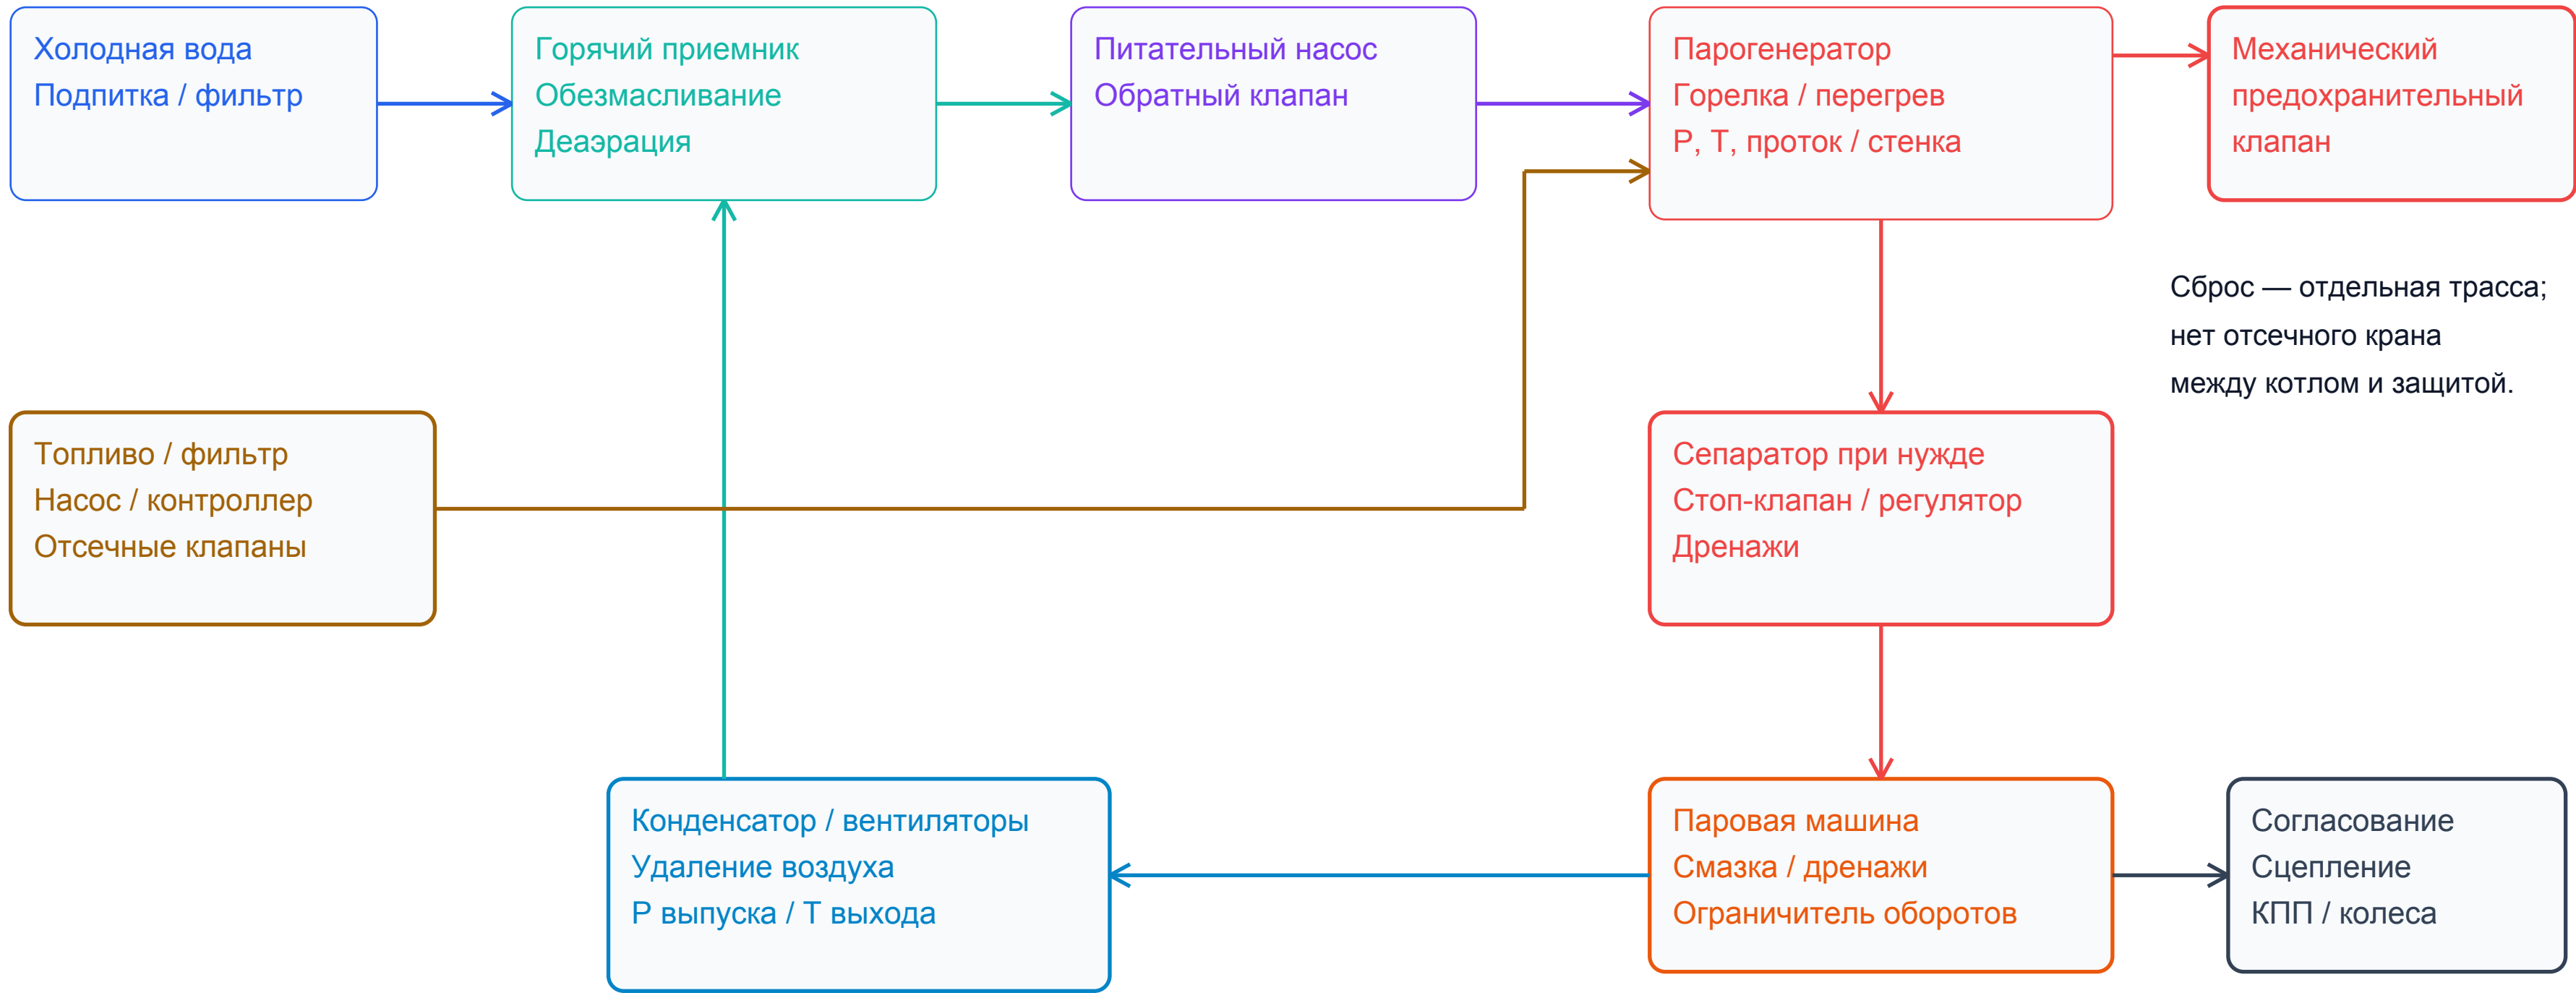

Отвод продуктов сгорания — отдельный тракт. Пар, дым и горячая вода не проходят в салон.

Параметры соединений, сечения кабелей, уставки защиты и диаметры труб требуют отдельного рабочего проекта.